


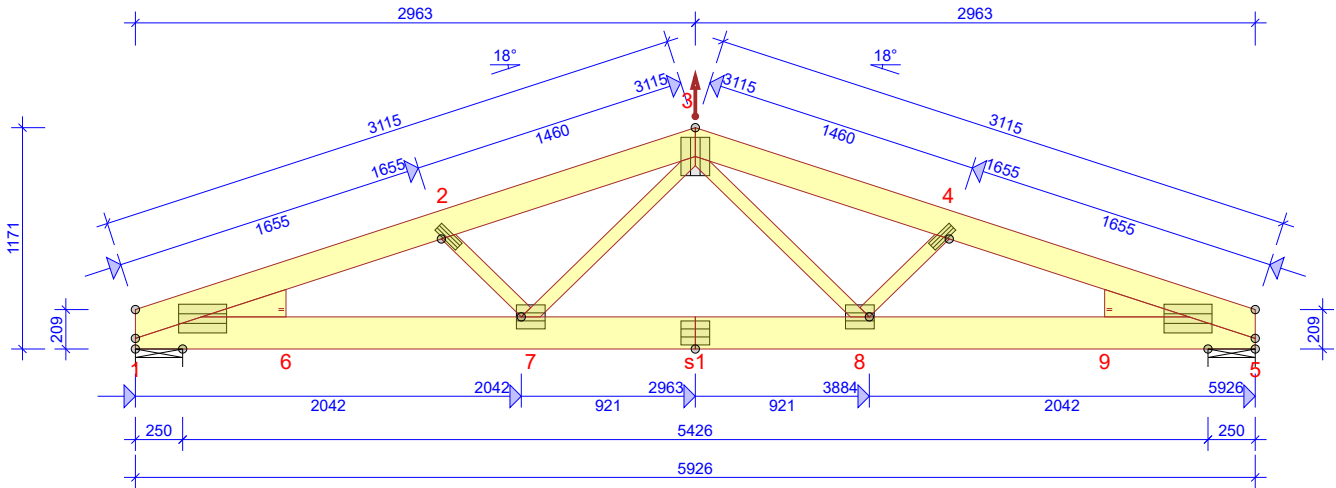

ALLMÄNNA ANVISNINGAR

KONSTRUKTIONEN HAR BERÄKNATS MED
DATAPROGRAM "MITEK PAMIR",
OBOS Bostadsutveckling AB - LIC.NR: 1514
DIM. NORM: EN 1995-1-1:2004 + A2:2014 + EKS 12
FULLSTÄNDIGA RESULTAT ENL. BERÄKNINGSUTSKRIFT

GENERELLA UPPGIFTER

MATERIALBREDD (mm):	45
VIKT (kg/st):	50
LASTBREDD MAX (mm):	1200
LASTFÖRDELNINGSAKTOR:	1,1
SÄKERHETSKLASS:	SK2
KLIMATKLASS:	2 = 65% <= RF < 85%
AVSTYVNINGAR: SE TVÄRSNITTSTABELL	

BELASTNINGAR (kN/m²)

SNÖLAST (Sk, 400 m.ö.h.):	2,5
VINDLAST (qp(z)):	0,85
NYTTIG LAST PÅ UNDERRAM:	0,5
EGENLAST PÅ YTTERTAK:	0,65
EGENLAST PÅ INNERTAK:	0,3

UPPLAGSREAKTIONER BROTTGR. (kN)

KNUT NR	RIKTN.	LK P/L MAX	LK M MAX	LK K/MO MAX	LK K/MO MIN	U-BR mm
1	HOR.	0	0	-1,16	-	
1	VER.	4,19	16,09	14,45	-1,48	30
5	VER.	4,19	16,09	14,45	-1,48	30

MAX DEFORMATION I BRUKSGRÄNS (mm)

KNUT NR	VER.	HOR.	LK NR.
s1	8,1	0,6	1001:5:1 (WINST)
s1-7	8	0,6	1001:5:1 (WINST)
5	-0,1	1,6	1001:6:1 (WINST)
FÖR DEFORMATION I FLER PUNKTER - SE BER.UTSKRIFT			


TOLERANS FÖRBANDSPACERING: 8 mm

TVÄRSNITT BREDD 45 mm				
KONSTR. DEL	HÖJD mm	KVALITET	AVSTYV. mm/st	NG. %
1-3	145	C24	800	74
3-5	145	C24	800	74
1-5	170	C24	FULL	53
5-9	145	C24		3
2-7	70	C18	INGEN	24
3-7	70	C18	INGEN	47
3-8	70	C18	INGEN	47
4-8	70	C18	INGEN	24
1-6	145	C24		3

FÖRBAND - EXKL. SKARVAR				
KNUT NR	FÖRB. LITT	BREDD mm	LÄNGD mm	NG. %
1	M20H	152	254	80
2	M20H	51	152	42
3	M20H	152	203	71
4	M20H	51	152	42
5	M20H	152	254	80
7	M20H	127	152	58
8	M20H	127	152	58

FÖRBAND - SKARVAR				
KNUT NR	FÖRB. LITT	BREDD mm	LÄNGD mm	NG. %
s1	M20H	127	152	87


© Ritningen är skyddad enligt upphovsrättslagen och får inte kopieras, spridas eller i övrigt användas utan upphovsmannens medgivande.

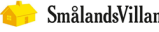

OBOS BOSTADSUTVECKLING AB
ART NR: ES019IL-2
TAKFOT INKLÄDD LÅNG 950mm -2 KAPADE TASSAR 687
HUSVÄGG 250 + SIDOB. 120 SKALA 1:40 SIDA 1/1

RITAD/KONSTR. AV RNM
GRANSK
ARBETSNR. ES019IL-2
Stockholm. 2024-08-13
2024.2b (e327eed)

KOD TYP POS
ES019IL-2
RITNINGNUMMER
ES019IL-2
REV.

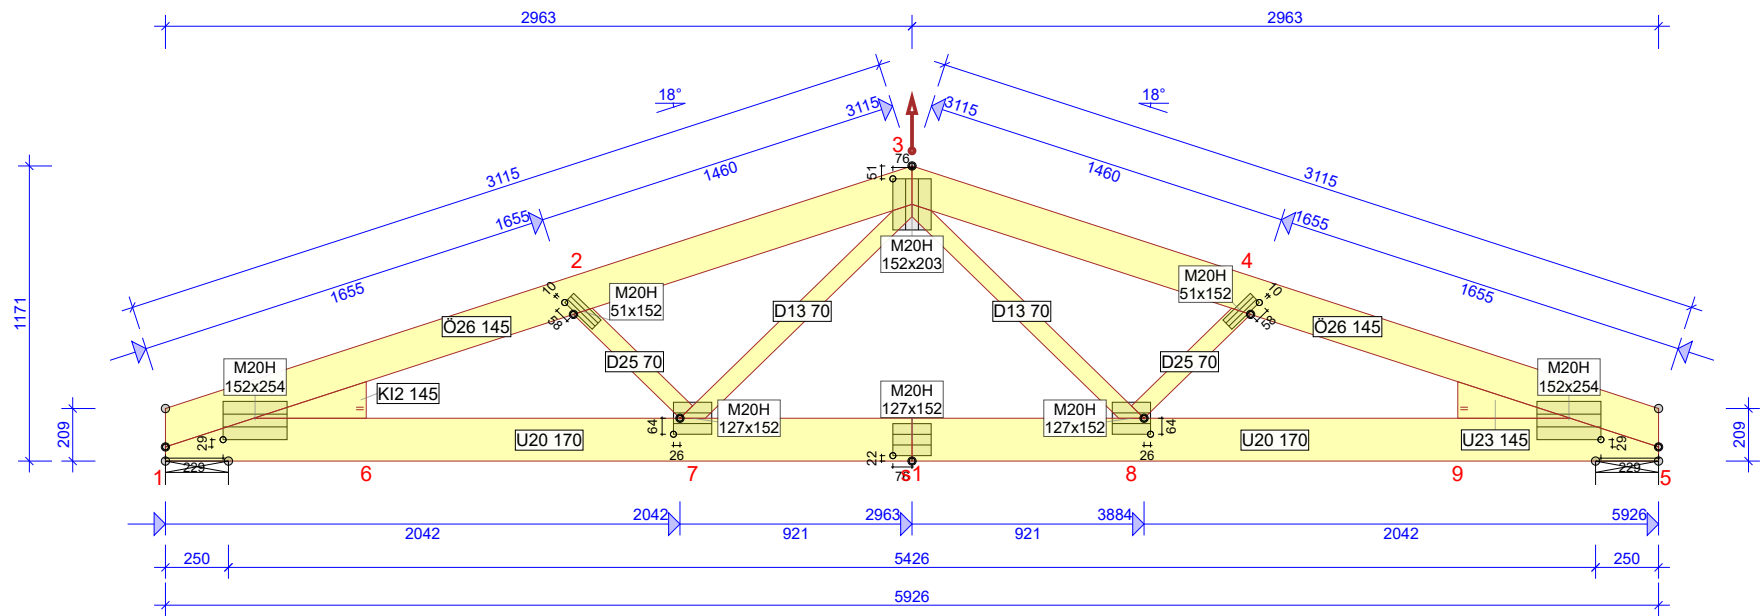

TOLERANS FÖRBANDSPACERING: 8 mm

2024-08-13 - 11:13
2024.2b (e327eed)

ARBETSNR.
ES019IL-2

KOD TYP POS

ES019IL-2

RITNINGSNUMMER

ES019IL-2

GRANSKAD AV: *JR*
RITAD/KONSTR. AV: RNM

OBOS BOSTADSUTVECKLING AB


ART NR: ES019IL-2

PRODUKTIONSRTNING


SIDA 1/1

TAKFOT INKLÄDD LÄNG 950mm -2 KAPADE TASSAR 687 REV.


HUSVÄGG 250 + SIDOB. 120

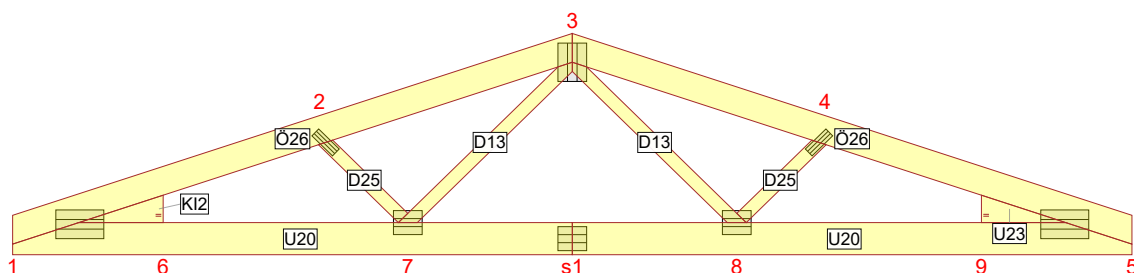**ÖVERRAM - Ö26**


1-3	Dim./Kval	45 x 145 mm C24
5-3	Total längd:	3163 mm
	ÖK / C / UK:	3115 / 3115 / 3115 mm
	Antal per konstruktion:	2 st
	Antal totalt:	2 st(1v,1h)

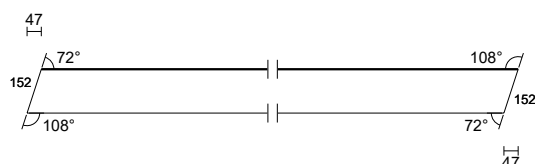**UNDERRAM - U20**


s1-5	Dim./Kval	45 x 170 mm C24
1-s1	Total längd:	2963 mm
	ÖK / C / UK:	2612 / 2874 / 2963 mm
	Antal per konstruktion:	2 st
	Antal totalt:	2 st(1v,1h)

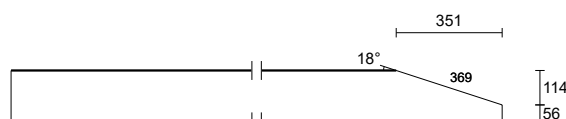**UNDERRAM - U23**


9-5	Dim./Kval	45 x 145 mm C24
	Total längd:	446 mm
	ÖK / C / UK:	0 / 223 / 446 mm
	Antal per konstruktion:	1 st
	Antal totalt:	1 st(1h)

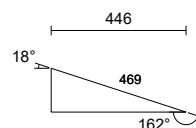**DIAGONAL - D13**


3-7	Dim./Kval	45 x 70 mm C18
3-8	Total längd:	1252 mm
	ÖK / C / UK:	1181 / 1216 / 1146 mm
	Antal per konstruktion:	2 st
	Antal totalt:	2 st(1v,1h)

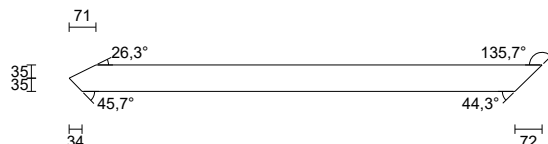**DIAGONAL - D25**

2-7	Dim./Kval	45 x 70 mm C18
4-8	Total längd:	592 mm
	ÖK / C / UK:	591 / 573 / 556 mm
	Antal per konstruktion:	2 st
	Antal totalt:	2 st(1v,1h)

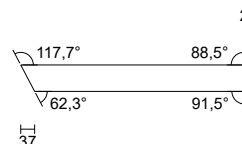**KIL - K12**

1-6	Dim./Kval	45 x 145 mm C24
	Total längd:	446 mm
	ÖK / C / UK:	0 / 223 / 446 mm
	Antal per konstruktion:	1 st
	Antal totalt:	1 st(1v)

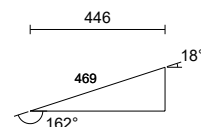

ARBETSNR.

ES019IL-2

GRANSKAD AV:

RITAD/KONSTR. AV: RNM

KAPLISTA

SIDA 1/1

2024-08-13 - 11:13
2024.2b (e327eed)

KOD TYP POS

RITNINGSNUMMER

OBOS BOSTADSUTVECKLING AB


TAKFOT INKLÄDD LÄNG 950mm -2 KAPADE TASSAR 687 REV.

ES019IL-2**ES019IL-2**


ART NR: ES019IL-2

HUSVÄGG 250 + SIDOB. 120


ES019IL-2

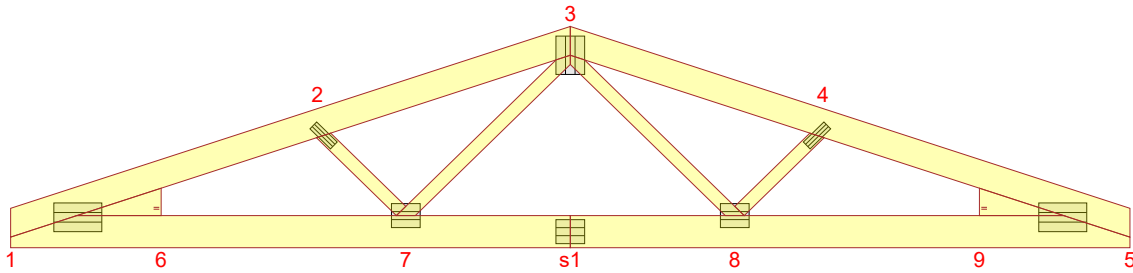

1 / 5

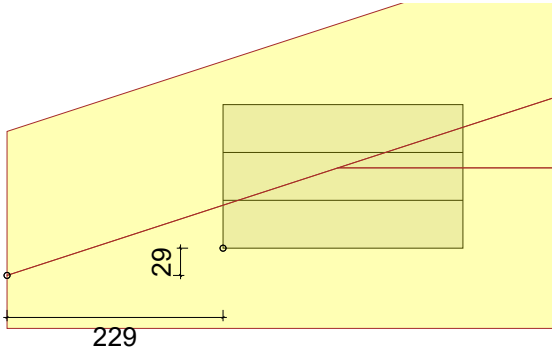

2 / 4

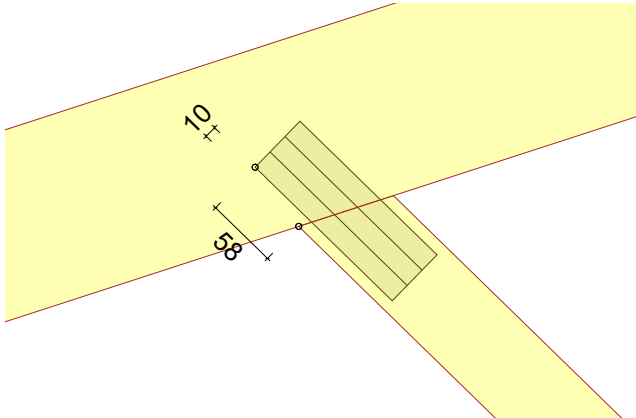


M20H 152x254

80% M20H 51x152

42%

3

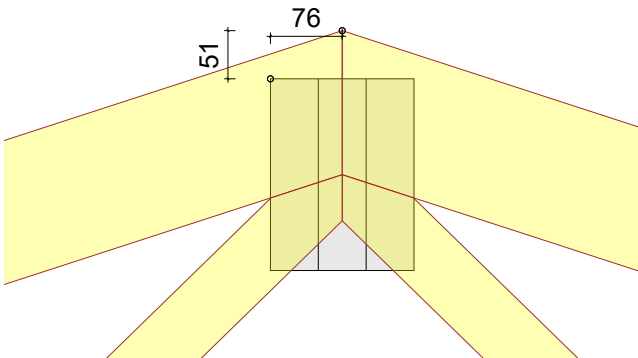


M20H 152x203


71% M20H 127x152

58%

7 / 8

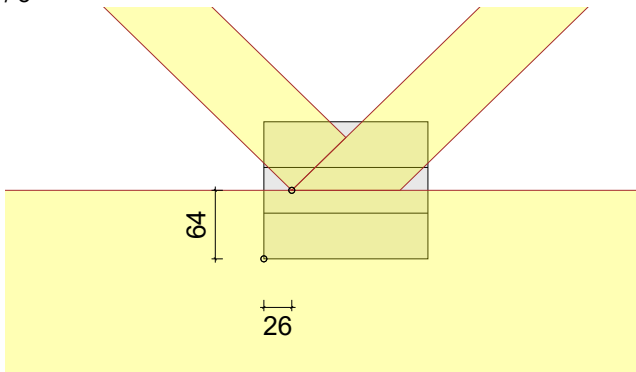

s1

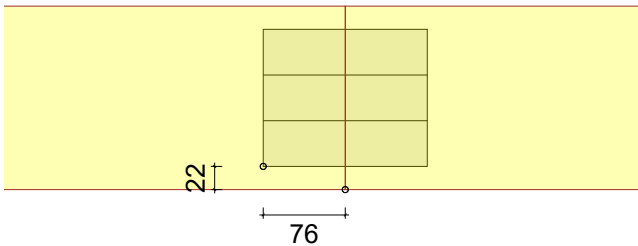

M20H 127x152

87%

TOLERANS FÖRBANDSPACERING: 8 mm

ARBETSNR.
ES019IL-2

GRANSKAD AV: *JK*
RITAD/KONSTR. AV: RNM

SPIKPLÅTAR

SIDA 1/1

2024-08-13 - 11:13
2024.2b (e327eed)

KOD TYP POS
ES019IL-2

RITNINGSNUMMER | OBOS BOSTADSUTVECKLING AB
ES019IL-2 ART NR: ES019IL-2

TAKFOT INKLÄDD LÅNG 950mm -2 KAPADE TASSAR 687 REV.
HUSVÄGG 250 + SIDOB. 120