

ALLMÄNNA ANVISNINGAR

KONSTRUKTIONEN HAR BERÄKNATS MED
DATAPROGRAM "MITEK PAMIR",
OBOS Bostadsutveckling AB - LIC.NR: 1514
DIM. NORM: EN 1995-1-1:2004 + A2:2014 + EKS 12
FULLSTÄNDIGA RESULTAT ENL. BERÄKNINGSUTSKRIFT

GENERELLA UPPGIFTER

MATERIALBREDD (mm): 45
VIKT (kg/st): 50
LASTBREDD MAX (mm): 1200
LASTFÖRDELNINGSAKTOR: 1,1
SÄKERHETSKLASS: SK2
KLIMATKLASS: 2 = 65% <= RF < 85%
AVSTYVNINGAR: SE TVÄRSNITTSTABELL

BELASTNINGAR (kN/m²)


SNÖLAST (Sk, 400 m.ö.h.): 2,5
VINDLAST (qp(z)): 0,85
NYTTIG LAST PÅ UNDERRAM: 0,5
EGENLAST PÅ YTERTAK: 0,65
EGENLAST PÅ INNERTAK: 0,3

UPPLAGSREAKTIONER BROTTGR. (kN)

KNUT NR	RIKTN.	LK P/L MAX	LK M MAX	LK K/MO MAX	LK K/MO MIN	U-BR mm
1	HOR.	0	0	1,15	-	
1	VER.	4,16	16	14,37	-1,48	30
5	VER.	4,14	15,8	14,22	-1,45	29

MAX DEFORMATION I BRUKSGRÄNS (mm)

KNUT NR	VER.	HOR.	LK NR.
s1	7,9	0,6	1001:5:1 (WINST)
s1-7	7,9	0,6	1001:5:1 (WINST)
5	0	1,5	1001:5:1 (WINST)
FÖR DEFORMATION I FLER PUNKTER - SE BER.UTSKRIFT			

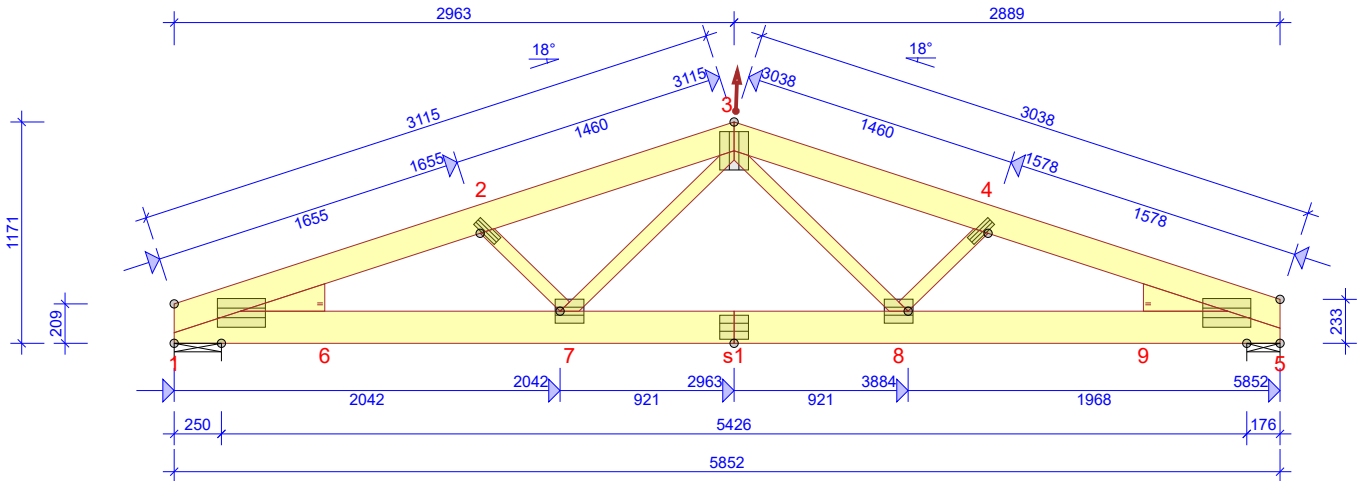

TOLERANS FÖRBANDSPACERING: 8 mm

TVÄRSNITT BREDD 45 mm				
KONSTR. DEL	HÖJD mm	KVALITET	AVSTYV. mm/st	NG. %
1-3	145	C24	800	74
3-5	145	C24	800	76
1-5	170	C24	FULL	53
1-6	145	C24		3
5-9	145	C24		3
2-7	70	C18	INGEN	24
3-7	70	C18	INGEN	47
3-8	70	C18	INGEN	45
4-8	70	C18	INGEN	24

FÖRBAND - EXKL. SKARVAR				
KNUT NR	FÖRB. LITT	BREDD mm	LÄNGD mm	NG. %
1	M20H	152	254	80
2	M20H	51	152	42
3	M20H	152	203	72
4	M20H	51	152	42
5	M20H	152	254	78
7	M20H	127	152	59
8	M20H	127	152	55

FÖRBAND - SKARVAR				
KNUT NR	FÖRB. LITT	BREDD mm	LÄNGD mm	NG. %
s1	M20H	127	152	87

© Ritningen är skyddad enligt upphovsrättslagen och får inte kopieras, spridas eller i övrigt användas utan upphovsmannens medgivande.



OBOS BOSTADSUTVECKLING AB
ART NR: ES019IL-3
TAKFOT INKLÄDD LÅNG 950mm -3 KAPADE TASSAR 687+761
HUSVÄGG 250

SKALA 1:40
SIDA 1/1


RITAD/KONSTR. AV RNM
Stockholm. 2024-08-13
2024.2b (e327eed)

GRANSK
ARBETSNR. ES019IL-3

KOD TYP POS
ES019IL-3

RITNINGSNUMMER
ES019IL-3

REV.

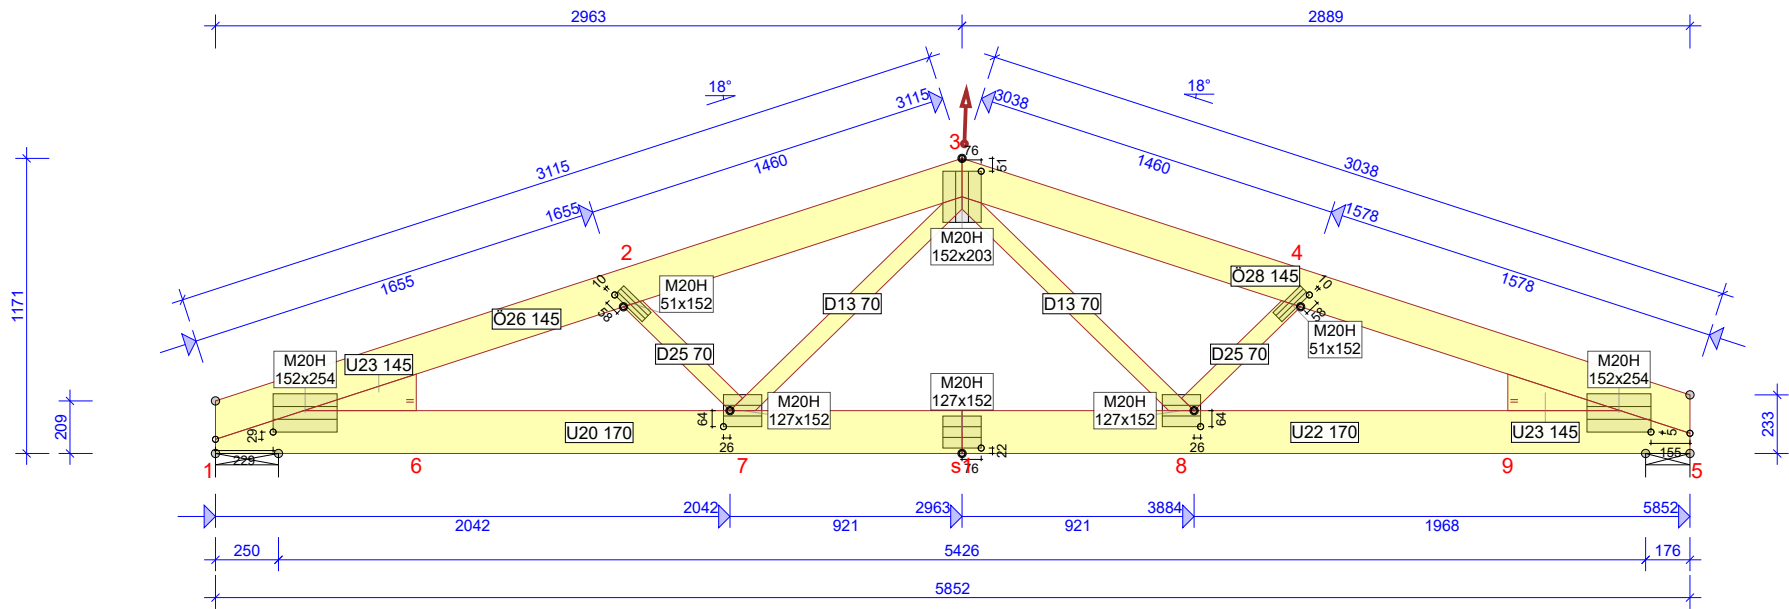

TOLERANS FÖRBANDSPACERING: 8 mm

2024-08-13 - 11:13
2024.2b (e327eed)

ARBETSNR.
ES019IL-3

KOD TYP POS

ES019IL-3

RITNINGSNUMMER

ES019IL-3

GRANSKAD AV: *JR*
RITAD/KONSTR. AV: RNM


OBOS BOSTADSUTVECKLING AB

ART NR: ES019IL-3

PRODUKTIONSRTNING


SIDA 1/1

TAKFOT INKLÄDD LÅNG 950mm - 3 KAPADE TASSAR 687+761
HUSVÄGG 250

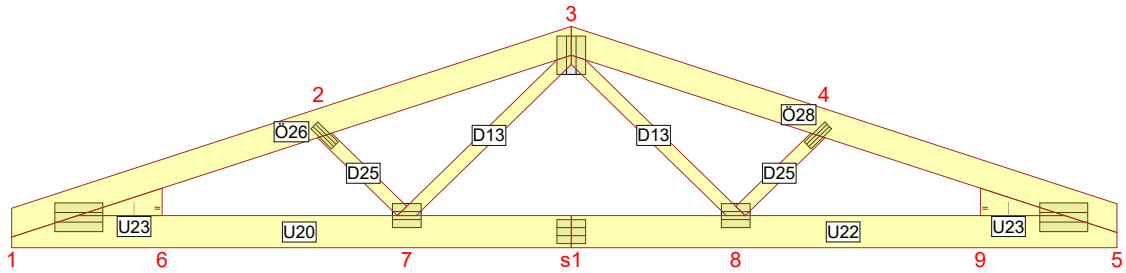


ÖVERRAM - Ö26

1-3	Dim./Kval	45 x 145 mm C24
	Total längd:	3163 mm
	ÖK / C / UK:	3115 / 3115 / 3115 mm
	Antal per konstruktion:	1 st
	Antal totalt:	1 st(1v)

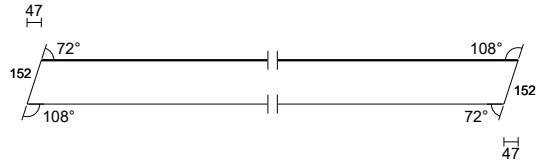

ÖVERRAM - Ö28

3-5	Dim./Kval	45 x 145 mm C24
	Total längd:	3085 mm
	ÖK / C / UK:	3038 / 3038 / 3038 mm
	Antal per konstruktion:	1 st
	Antal totalt:	1 st(1h)

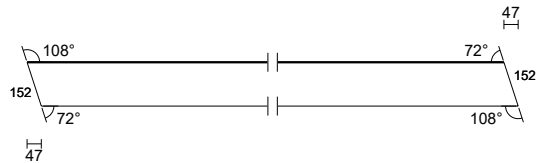


UNDERRAM - U20

1-s1	Dim./Kval	45 x 170 mm C24
	Total längd:	2963 mm
	ÖK / C / UK:	2612 / 2874 / 2963 mm
	Antal per konstruktion:	1 st
	Antal totalt:	1 st(1v)




UNDERRAM - U22

s1-5	Dim./Kval	45 x 170 mm C24
	Total längd:	2889 mm
	ÖK / C / UK:	2612 / 2874 / 2889 mm
	Antal per konstruktion:	1 st
	Antal totalt:	1 st(1h)

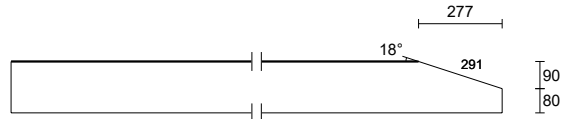


UNDERRAM - U23

1-6	Dim./Kval	45 x 145 mm C24
9-5	Total längd:	446 mm
	ÖK / C / UK:	0 / 223 / 446 mm
	Antal per konstruktion:	2 st
	Antal totalt:	2 st(1v,1h)

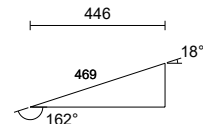


DIAGONAL - D13

3-7	Dim./Kval	45 x 70 mm C18
3-8	Total längd:	1252 mm
	ÖK / C / UK:	1181 / 1216 / 1146 mm
	Antal per konstruktion:	2 st
	Antal totalt:	2 st(1v,1h)

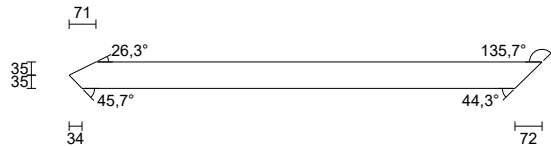

DIAGONAL - D25

2-7	Dim./Kval	45 x 70 mm C18
4-8	Total längd:	592 mm
	ÖK / C / UK:	591 / 573 / 556 mm
	Antal per konstruktion:	2 st
	Antal totalt:	2 st(1v,1h)

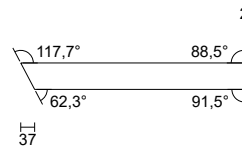

ARBETSNR.

ES019IL-3

GRANSKAD AV:

RITAD/KONSTR. AV: RNM

KAPLISTA

SIDA 1/1

2024-08-13 - 11:13
2024.2b (e327eed)

KOD TYP POS

RITNINGSNUMMER

ES019IL-3


ES019IL-3

OBOS BOSTADSUTVECKLING AB

ART NR: ES019IL-3

TAKFOT INKLÄDD LÅNG 950mm -3 KAPADE TASSAR 687+761 REV.

HUSVÄGG 250

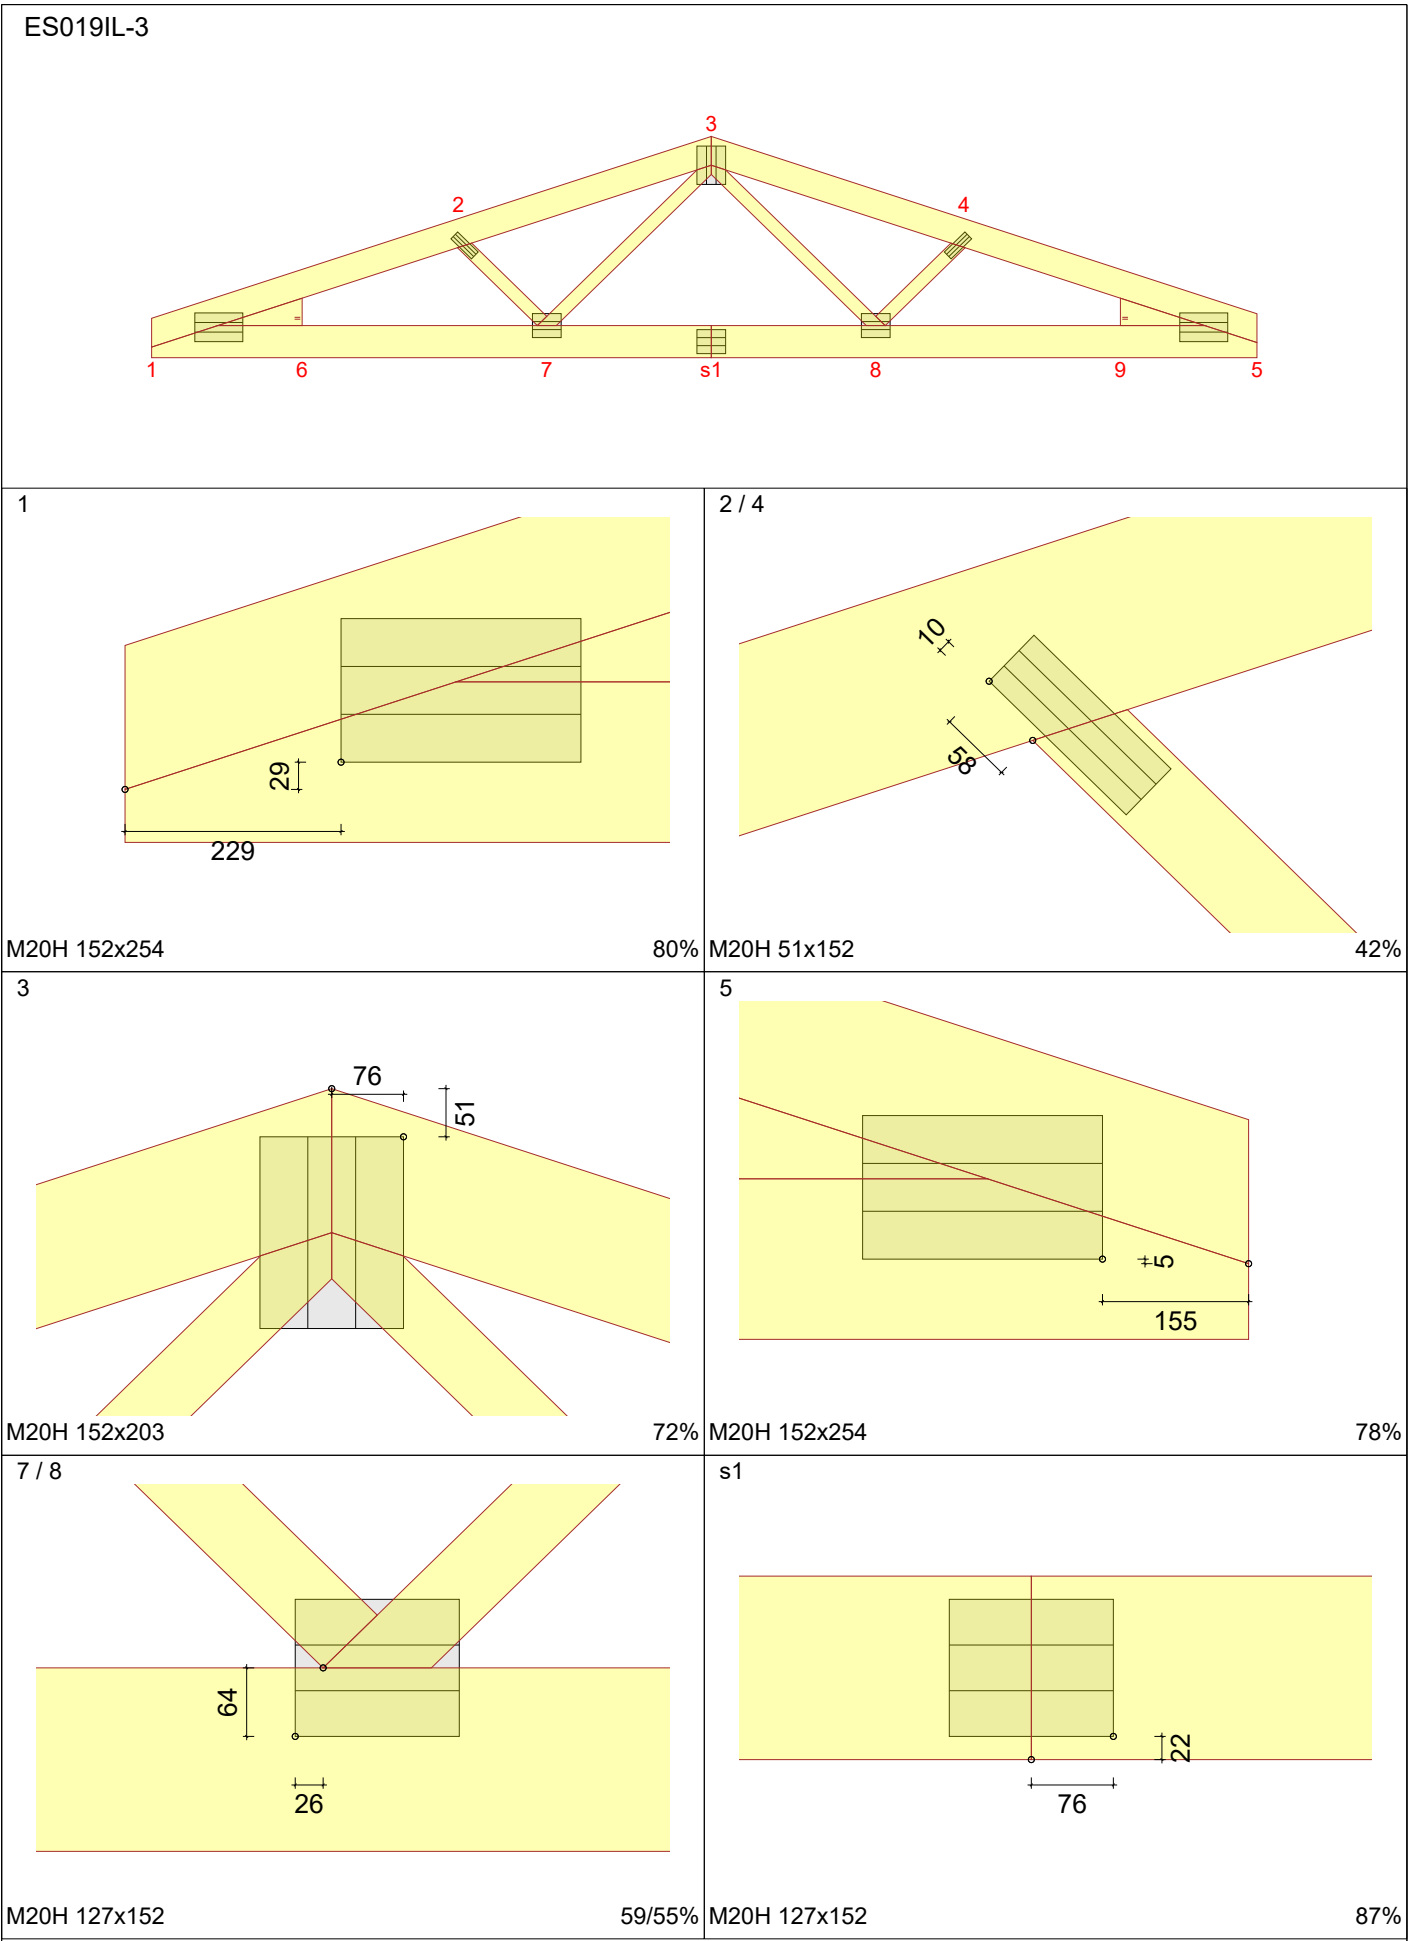

TOLERANS FÖRBANDSPACERING: 8 mm		ARBETSNR. ES019IL-3	GRANSKAD AV: <i>JK</i> RITAD/KONSTR. AV: RNM	SPIKPLÅTAR	SIDA 1/1
2024-08-13 - 11:13 2024.2b (e327eed)	KOD TYP POS ES019IL-3	RITNINGSNUMMER ES019IL-3	OBOS BOSTADSUTVECKLING AB ART NR: ES019IL-3	TAKFOT INKLÄDD LÅNG 950mm -3 KAPADE TASSAR 687+761 HUSVÄGG 250	REV.