


AVSTYVNINGAR ENLIGT TVÄRSNITTSTABELL (KOLUMN AVSTYV.) OCH TAKSTOLSYSTEMETS STABILITET SKA DIMENSIONERAS SEPARAT.

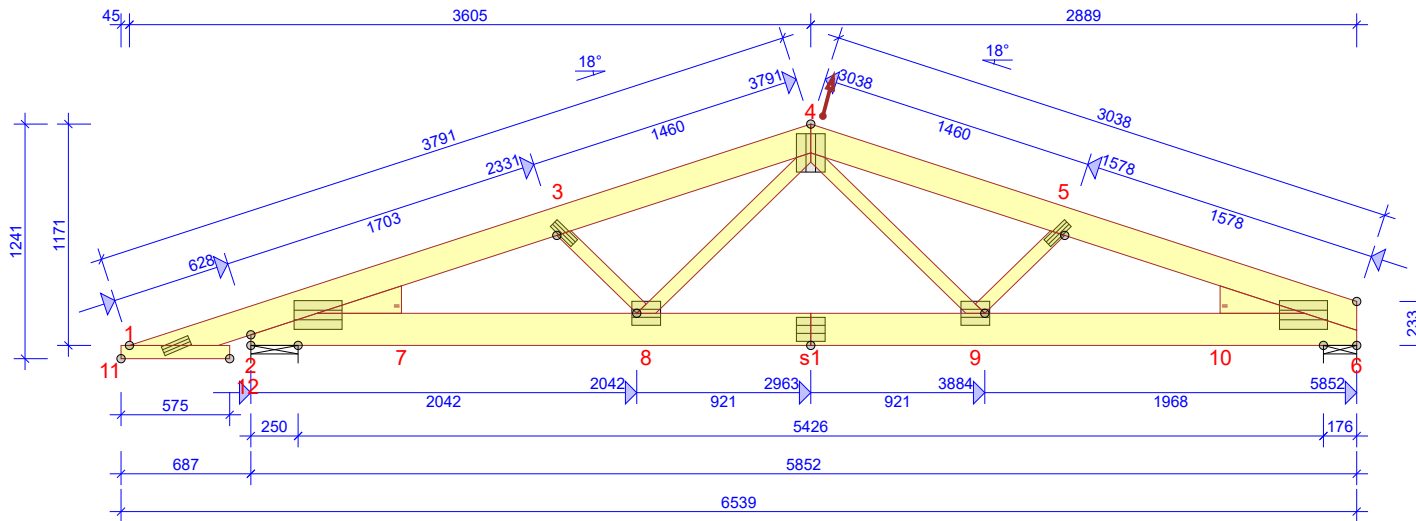

KONSTRUKTIONEN HAR BERÄKNATS MED
DATAPROGRAM "MITEK PAMIR",
OBOS Bostadsutveckling AB - LIC.NR: 1514
DIM. NORM: EN 1995-1-1:2004 + A2:2014 + EKS 12
FULLSTÄNDIGA RESULTAT ENL. BERÄKNINGSUTSKRIFT

MATERIALBREDD (mm):	45
VIKT (kg/st):	52
LASTBREDD MAX (mm):	1200
LASTFÖRDELNINGSAKTOR:	1,1
SÄKERHETSKLASS:	SK2
KLIMATKLASS:	2 = 65% <= RF < 85%
AVSTYVNINGAR: SE TVÄRSNITTSTABELL	

SNÖLAST (Sk, 400 m.ö.h.):	2,5
VINDLAST (qp(z)):	0,85
NYTTIG LAST PÅ UNDERRAM:	0,5
EGENLAST PÅ YTTERTAK:	0,65
EGENLAST PÅ INNERTAK:	0,3

KNUT NR	RIKTN. HOR.	LK P/L MAX	LK M MAX	LK K/MO MAX	LK K/MO MIN	U-BR mm
2	HOR.	0	0	1,27	-	
2	VER.	5,18	20,03	17,66	-1,86	49
6	VER.	4,06	15,54	13,96	-1,5	28

KNUT NR	VER.	HOR.	LK NR.
s1	7,9	0,7	1001:6:1 (WINST)
s1-8	7,8	0,6	1001:5:1 (WINST)
6	0	1,4	1001:6:1 (WINST)

FÖR DEFORMATION I FLER PUNKTER - SE BER.UTSKRIFT

TVÄRSNITT		BREDD 45 mm		
KONSTR. DEL	HÖJD mm	KVALITET	AVSTYV. mm/st	NG. %
4-6	145	C24	800	74
1-4	145	C24	800	91
2-6	170	C24	FULL	64
2-7	145	C24		2
6-10	145	C24		3
11-12	70	C18	INGEN	12
3-8	70	C18	INGEN	23
4-8	70	C18	INGEN	41
4-9	70	C18	INGEN	46
5-9	70	C18	INGEN	24

FÖRBAND - EXKL. SKARVAR				
KNUT NR	FÖRB. LITT	BREDD mm	LÄNGD mm	NG. %
1	M20H	51	152	59
2	M20H	152	254	86
3	M20H	51	152	42
4	M20H	152	203	72
5	M20H	51	152	42
6	M20H	152	254	76
8	M20H	127	152	55
9	M20H	127	152	56


FÖRBAND - SKARVAR				
KNUT NR	FÖRB. LITT	BREDD mm	LÄNGD mm	NG %
s1	M20H	127	152	80

© Ritningen är skyddad enligt upphovsrättslagen och får inte kopieras, spridas eller i övrigt användas utan upphovsmannens medgivande.

 		OBOS BOSTADSUTVECKLING AB ART NR: ES019IL-4	
		TAKFOT INKLÄDD LÅNG 950mm -4 KAPAD TASS 761 HUSVÄGG 250	
RITAD/KONSTR. AV RNM	GRANSK 	ARBETSNR. ES019IL-4	SKALA 1:40 SIDA 1/1
Stockholm, 2024-08-13 		KOD TYP POS ES019IL-4	RITNINGSNUMMER ES019IL-4 REV.




HUSVÄGG 250

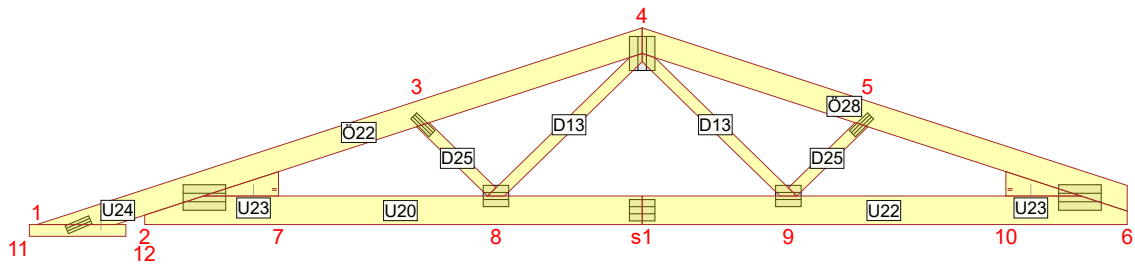


ÖVERRAM - Ö22

1-4	Dim./Kval	45 x 145 mm C24
	Total längd:	3791 mm
	ÖK / C / UK:	3791 / 3544 / 3298 mm
	Antal per konstruktion:	1 st
	Antal totalt:	1 st(1v)

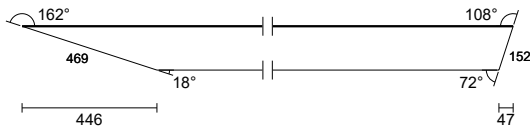

ÖVERRAM - Ö28

4-6	Dim./Kval	45 x 145 mm C24
	Total längd:	3085 mm
	ÖK / C / UK:	3038 / 3038 / 3038 mm
	Antal per konstruktion:	1 st
	Antal totalt:	1 st(1h)

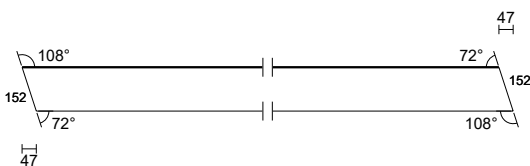


UNDERRAM - U20

2-s1	Dim./Kval	45 x 170 mm C24
	Total längd:	2963 mm
	ÖK / C / UK:	2612 / 2874 / 2963 mm
	Antal per konstruktion:	1 st
	Antal totalt:	1 st(1v)




UNDERRAM - U22

s1-6	Dim./Kval	45 x 170 mm C24
	Total längd:	2889 mm
	ÖK / C / UK:	2612 / 2874 / 2889 mm
	Antal per konstruktion:	1 st
	Antal totalt:	1 st(1h)

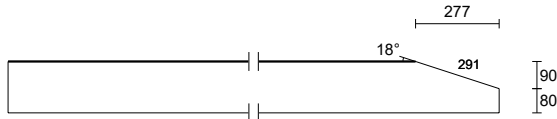

UNDERRAM - U23

2-7	Dim./Kval	45 x 145 mm C24
10-6	Total längd:	446 mm
	ÖK / C / UK:	0 / 223 / 446 mm
	Antal per konstruktion:	2 st
	Antal totalt:	2 st(1v,1h)

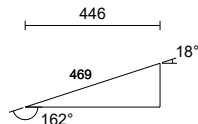


UNDERSPIKNING - U24

11-12	Dim./Kval	45 x 70 mm C18
	Total längd:	575 mm
	Antal per konstruktion:	1 st
	Antal totalt:	1 st(1v)



DIAGONAL - D13

4-8	Dim./Kval	45 x 70 mm C18
4-9	Total längd:	1252 mm
	ÖK / C / UK:	1181 / 1216 / 1146 mm
	Antal per konstruktion:	2 st
	Antal totalt:	2 st(1v,1h)

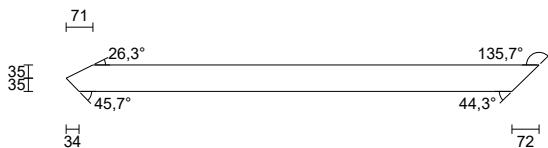

ARBETSNR.

ES019IL-4

GRANSKAD AV:

RITAD/KONSTR. AV: RNM

KAPLISTA

SIDA 1/2

2024-08-13 - 11:16
2024.2b (e327eed)


KOD TYP POS

ES019IL-4

RITNINGSNUMMER
ES019IL-4


OBOS BOSTADSUTVECKLING AB
ART NR: ES019IL-4

TAKFÖT INKLÄDD LÄNG 950mm -4 KAPAD TASS 761
HUSVÄGG 250

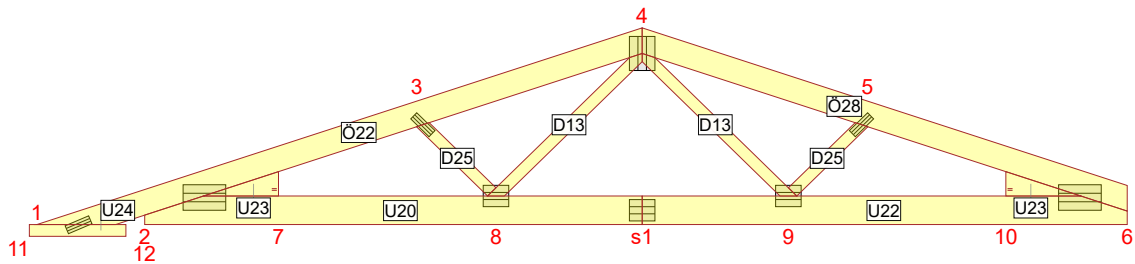

DIAGONAL - D25

3-8	Dim./Kval	45 x 70 mm C18
5-9	Total längd:	592 mm
	ÖK / C / UK:	591 / 573 / 556 mm
	Antal per konstruktion:	2 st
	Antal totalt:	2 st(1v,1h)

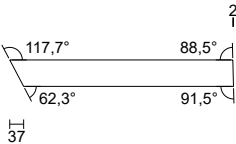

ARBETSNR.

ES019IL-4

GRANSKAD AV:

RITAD/KONSTR. AV: RNM

KAPLISTA

SIDA 2/2

2024-08-13 - 11:16
2024.2b (e327eed)

KOD TYP POS

ES019IL-4

RITNINGSNUMMER


ES019IL-4

OBOS BOSTADSUTVECKLING AB


ART NR: ES019IL-4

TAKFOT INKLÄDD LÄNG 950mm -4 KAPAD TASS 761
HUSVÄGG 250


ES019IL-4

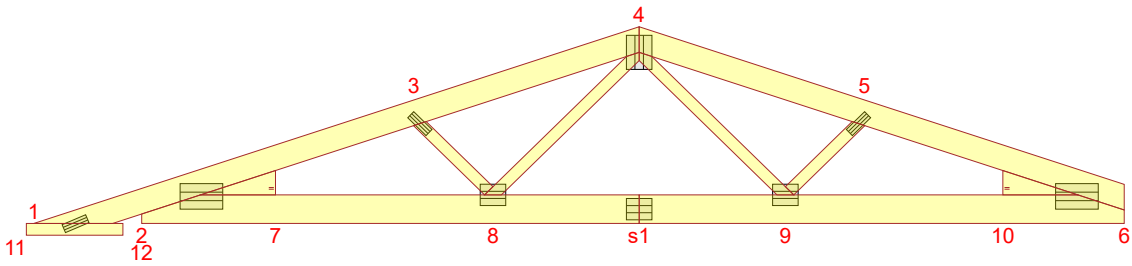

1

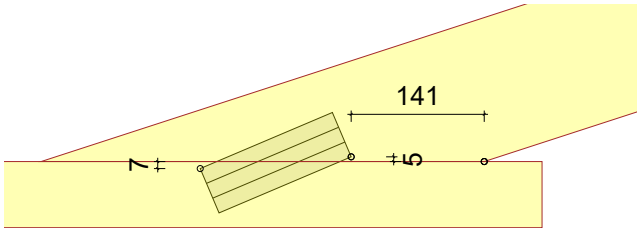

2

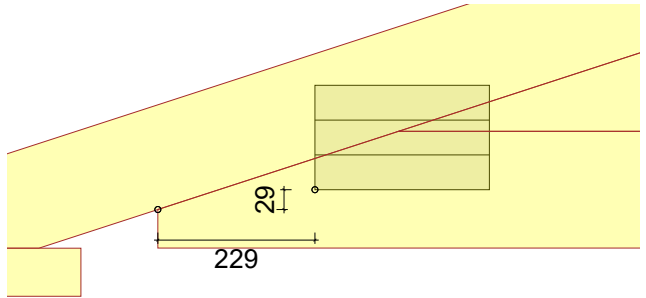


M20H 51x152

59%

M20H 152x254

86%


3 / 5

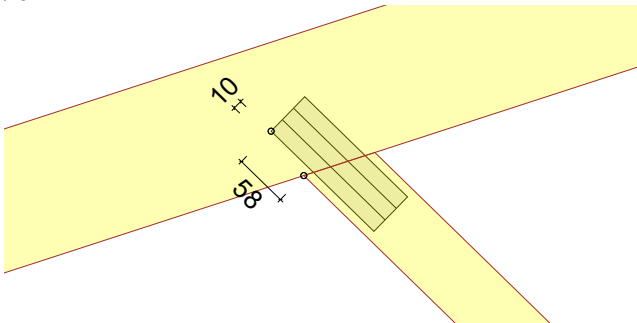

M20H 51x152

42%


4

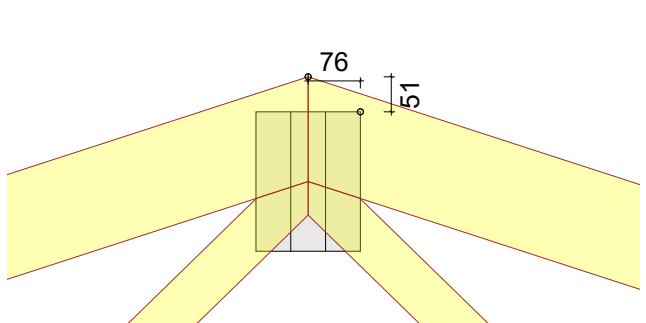

M20H 152x203

72%


6

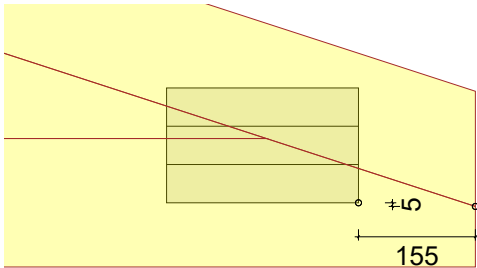

M20H 152x254

76%


8 / 9

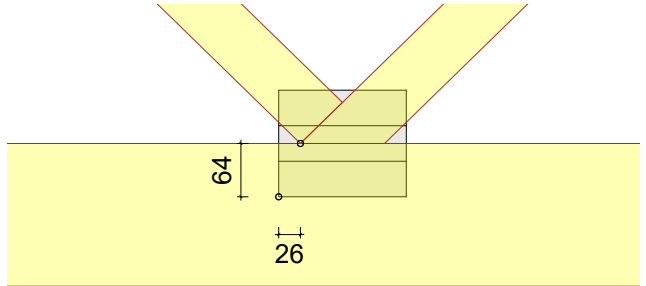

M20H 127x152

55/56%

s1

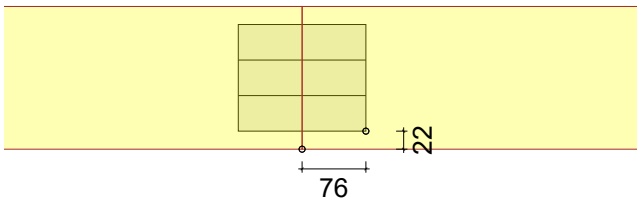

M20H 127x152

86%

TOLERANS FÖRBANDSPACERING: 8 mm

ARBETSNR.

ES019IL-4

GRANSKAD AV: *HR*

RITAD/KONSTR. AV: RNM

SPIKPLÅTAR

SIDA 1/1

2024-08-13 - 11:16
2024.2b (e327eed)

KOD TYP POS

ES019IL-4

RITNINGSNUMMER

ES019IL-4

OBOS BOSTADSUTVECKLING AB

ART NR: ES019IL-4

TAKFOT INKLÄDD LÄNG 950mm -4 KAPAD TASS 761 REV.
HUSVÄGG 250