


AVSTYVNINGAR ENLIGT TVÄRSNITTSTABELL (KOLUMN AVSTYV.) OCH TAKSTOLSYSTEMETS STABILITET SKA DIMENSIONERAS SEPARAT.

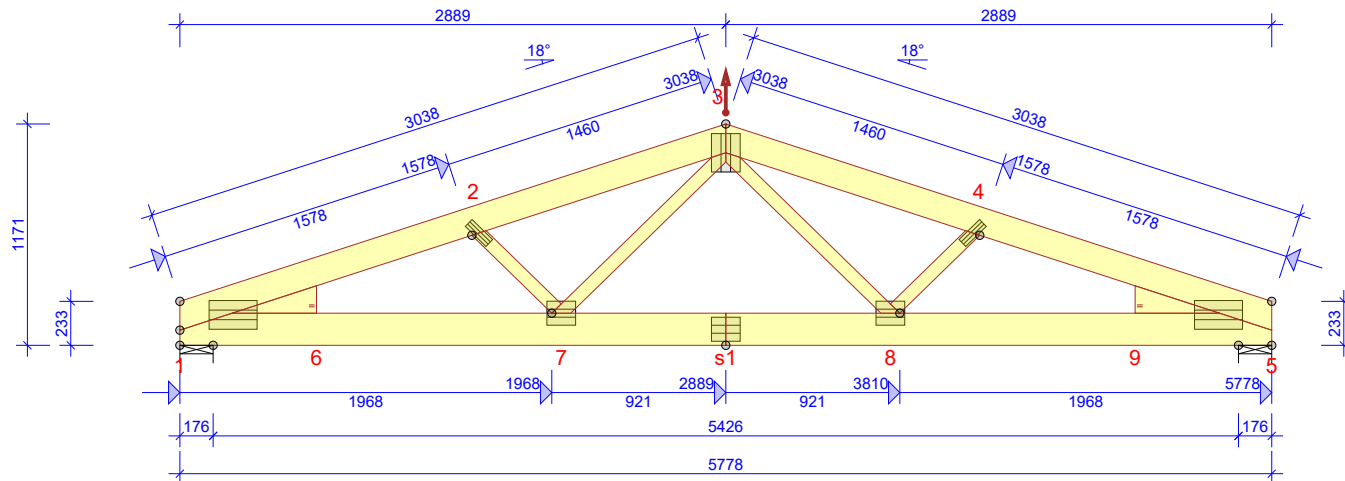

KONSTRUKTIONEN HAR BERÄKNATS MED
DATAPROGRAM "MITEK PAMIR",
OBOS Bostadsutveckling AB - LIC.NR: 1514
DIM. NORM: EN 1995-1-1:2004 + A2:2014 + EKS 12
FULLSTÄNDIGA RESULTAT ENL. BERÄKNINGSUTSKRIFT

MATERIALBREDD (mm):	45
VIKT (kg/st):	50
LASTBREDD MAX (mm):	1200
LASTFÖRDELNINGSAKTOR:	1,1
SÄKERHETSKLASS:	SK2
KLIMATKLASS:	2 = 65% <= RF < 85%
AVSTYVNINGAR: SE TVÄRSNITTSTABELL	

SNÖLAST (SK, 400 m.ö.h.):	2,5
VINDLAST (qp(z)):	0,85
NYTTIG LAST PÅ UNDERRAM:	0,5
EGENLAST PÅ YTTERTAK:	0,65
EGENLAST PÅ INNERTAK:	0,3

KNUT NR	RIKTN. HOR.	LK P/L MAX	LK M MAX	LK K/MO MAX	LK K/MO MIN	U-BR mm
1	HOR.	0	0	-1,14	-	
1	VER.	4,11	15,71	14,14	-1,44	29
5	VER.	4,11	15,71	14,14	-1,44	29

KNUT NR	VER.	HOR.	LK NR.
s1	7,8	0,6	1001:5:1 (WINST)
s1-7	7,8	0,6	1001:5:1 (WINST)
5	0	1,5	1001:6:1 (WINST)

FÖR DEFORMATION I FLER PUNKTER - SE BER.UTSKRIFT


TVÄRSNITT		BREDD 45 mm		
KONSTR. DEL	HÖJD mm	KVALITET	AVSTYV. mm/st	NG. %
1-3	145	C24	800	75
3-5	145	C24	800	75
1-5	170	C24	FULL	53
5-9	145	C24		3
2-7	70	C18	INGEN	24
3-7	70	C18	INGEN	45
3-8	70	C18	INGEN	45
4-8	70	C18	INGEN	24
1-6	145	C24		3

FÖRBAND - EXKL. SKARVAR				
KNUT NR	FÖRB. LITT	BREDD mm	LÄNGD mm	NG. %
1	M20H	152	254	77
2	M20H	51	152	42
3	M20H	152	203	70
4	M20H	51	152	42
5	M20H	152	254	77
7	M20H	127	152	56
8	M20H	127	152	56

FÖRBAND - SKARVAR				
KNUT NR	FÖRB. LITT	BREDD mm	LÄNGD mm	NG %
s1	M20H	127	152	8

© Ritningen är skyddad enligt upphovsrättslagen och får inte kopieras, spridas eller i övrigt användas utan upphovsmannens medgivande.

 		OBOS BOSTADSUTVECKLING AB ART NR: ES019IL-5 TAKFOT INKLÄDD LÅNG 950mm -5 KAPADE TASSAR 761 HUSVÄGG 250	
RITAD/KONSTR. AV RNM Stockholm. 2024-08-13	GRANSK 	ARBETS NR. ES019IL-5	SKALA 1:40 SIDA 1/1
KOD TYP POS ES019IL-5		RITNINGSSUMMER ES019IL-5	REV.

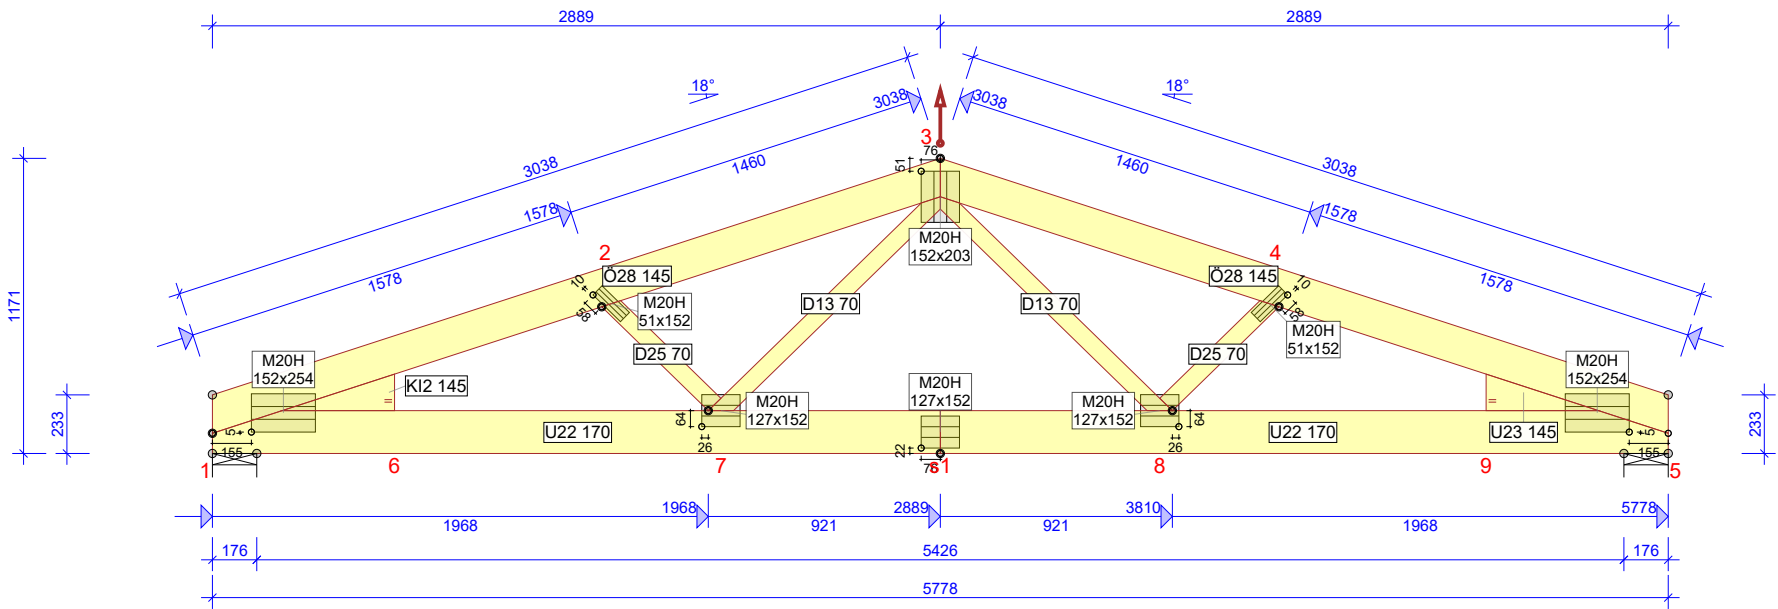

TOLERANS FÖRBANDSPACERING: 8 mm

2024-08-13 - 11:13
2024.2b (e327eed)

ARBETSNR.
ES019IL-5

KOD TYP POS

ES019IL-5

RITNINGSNUMMER

ES019IL-5

GRANSKAD AV: *JR*
RITAD/KONSTR. AV: RNM


OBOS BOSTADSUTVECKLING AB

ART NR: ES019IL-5

PRODUKTIONSRTNING


SIDA 1/1

TAKFÖT INKLÄDD LÅNG 950mm -5 KAPADE TASSAR 761
HUSVÄGG 250

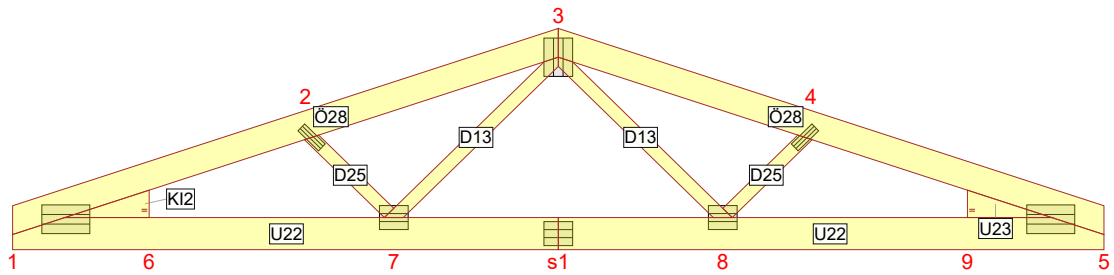


ÖVERRAM - Ö28

1-3	Dim./Kval	45 x 145 mm C24
5-3	Total längd:	3085 mm
	ÖK / C / UK:	3038 / 3038 / 3038 mm
	Antal per konstruktion:	2 st
	Antal totalt:	2 st(1v,1h)

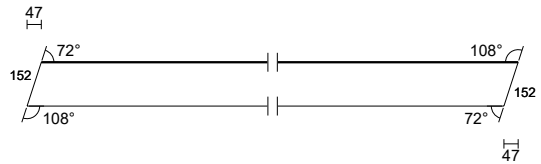


UNDERRAM - U22

s1-5	Dim./Kval	45 x 170 mm C24
1-s1	Total längd:	2889 mm
	ÖK / C / UK:	2612 / 2874 / 2889 mm
	Antal per konstruktion:	2 st
	Antal totalt:	2 st(1v,1h)

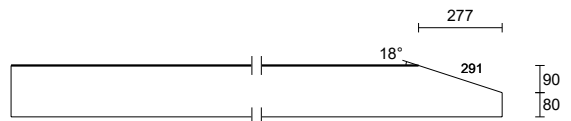


UNDERRAM - U23

9-5	Dim./Kval	45 x 145 mm C24
	Total längd:	446 mm
	ÖK / C / UK:	0 / 223 / 446 mm
	Antal per konstruktion:	1 st
	Antal totalt:	1 st(1h)

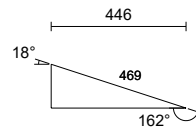


DIAGONAL - D13

3-7	Dim./Kval	45 x 70 mm C18
3-8	Total längd:	1252 mm
	ÖK / C / UK:	1181 / 1216 / 1146 mm
	Antal per konstruktion:	2 st
	Antal totalt:	2 st(1v,1h)

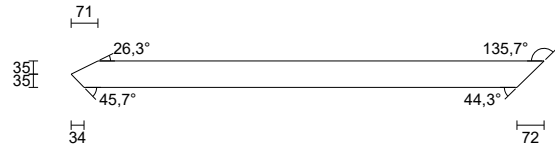


DIAGONAL - D25

2-7	Dim./Kval	45 x 70 mm C18
4-8	Total längd:	592 mm
	ÖK / C / UK:	591 / 573 / 556 mm
	Antal per konstruktion:	2 st
	Antal totalt:	2 st(1v,1h)

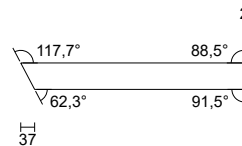

KIL - KI2

1-6	Dim./Kval	45 x 145 mm C24
	Total längd:	446 mm
	ÖK / C / UK:	0 / 223 / 446 mm
	Antal per konstruktion:	1 st
	Antal totalt:	1 st(1v)

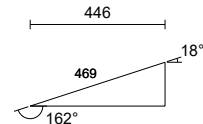

ARBETSNR.

ES019IL-5

GRANSKAD AV:

RITAD/KONSTR. AV: RNM

KAPLISTA

SIDA 1/1

2024-08-13 - 11:13
2024.2b (e327eed)

KOD TYP POS

ES019IL-5

RITNINGSNUMMER


ES019IL-5

OBOS BOSTADSUTVECKLING AB


ART NR: ES019IL-5

TAKFOT INKLÄDD LÄNG 950mm -5 KAPADE TASSAR 761
HUSVÄGG 250


ES019IL-5

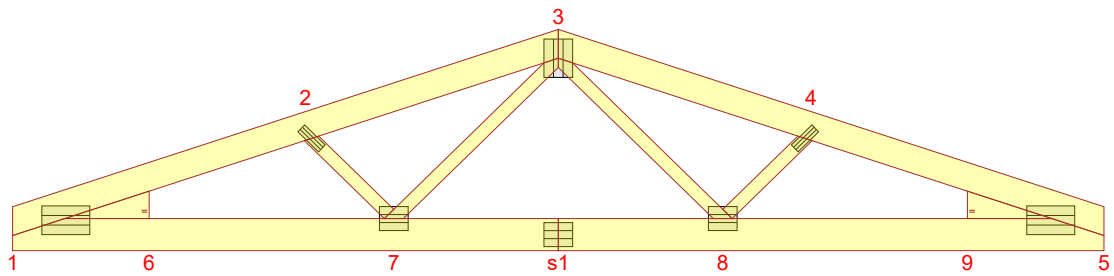

1 / 5

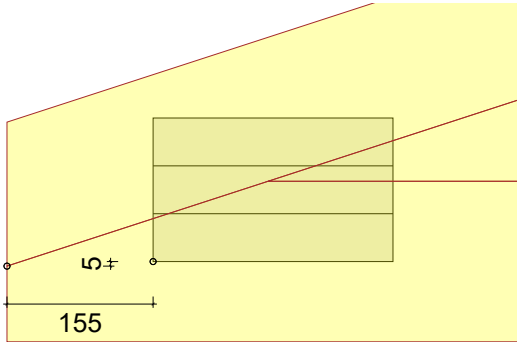

2 / 4

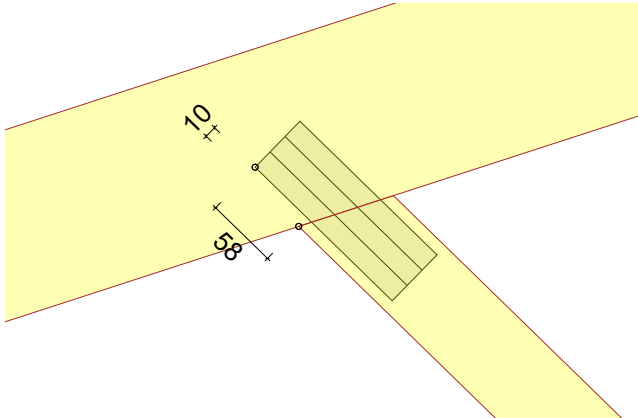


M20H 152x254


77% M20H 51x152

42%

3

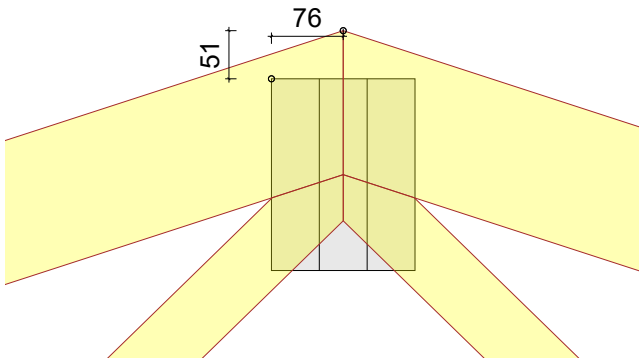

7 / 8

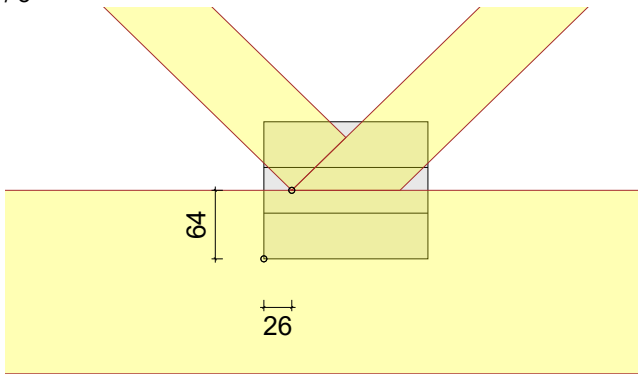


M20H 152x203

70% M20H 127x152

56%

s1

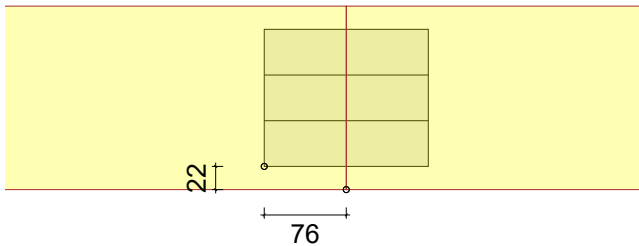

M20H 127x152

86%

TOLERANS FÖRBANDSPACERING: 8 mm

ARBETSNR.
ES019IL-5

GRANSKAD AV: *HR*
RITAD/KONSTR. AV: RNM

SPIKPLÅTAR

SIDA 1/1

2024-08-13 - 11:13
2024.2b (e327eed)

KOD TYP POS
ES019IL-5

RITNINGSNUMMER | OBOS BOSTADSUTVECKLING AB
ES019IL-5 ART NR: ES019IL-5

TAKFOT INKLÄDD LÅNG 950mm -5 KAPADE TASSAR 761 REV.
HUSVÄGG 250