

AVSTYVNINGAR ENLIGT TVÄRSNITTSTABELL (KOLUMN AVSTYV.) OCH TAKSTOLSYSTEMETS STABILITET SKA DIMENSIONERAS SEPARAT.



KONSTRUKTIONEN HAR BERÄKNATS MED
DATAPROGRAM "MITEK PAMIR",
OBOS Bostadsutveckling AB - LIC.NR: 1514
DIM. NORM: EN 1995-1-1:2004 + A2:2014 + EKS 12
FULLSTÄNDIGA RESULTAT ENL. BERÄKNINGSUTSKRIFT

MATERIALBREDD (mm):	45
VIKT (kg/st):	59
LASTBREDD MAX (mm):	1200
LASTFÖRDELNINGSAKTOR:	1,1
SÄKERHETSKLASS:	SK2
KLIMATKLASS:	2 = 65% <= RF < 85%
AVSTYVNINGAR: SE TVÄRSNITTSTABELL	

SNÖLAST (Sk, 400 m.ö.h.):	2,5
VINDLAST (qp(z)):	0,85
NYTTIG LAST PÅ UNDERRAM:	0,5
EGENLAST PÅ YTTERTAK:	0,65
EGENLAST PÅ INNERTAK:	0,3

KNUT NR	RIKTN. MAX	LK P/L MAX	LK M MAX	LK K/MO MAX	LK K/MO MIN	U-BR mm
2	HOR.	0	0	1,36	-	
2	VER.	5,64	21,85	19,31	-1,87	59
6	VER.	4,55	17,62	15,82	-1,67	36


KNUT NR	VER.	HOR.	LK NR.
s1	8,5	0,7	1001:5:1 (WINST)
s1-9	8,5	0,9	1001:6:1 (WINST)
6	-0,2	1,8	1001:6:1 (WINST)

FÖR DEFORMATION I FLER PUNKTER - SE BER.UTSKRIFT

TOLERANS FÖRBANDSPLACERING: 8 mm

© Ritningen är skyddad enligt upphovsrättslagen och får inte kopieras, spridas eller i övrigt användas utan upphovsmannens medgivande.

 		OBOS BOSTADSUTVECKLING AB ART NR: ES020IL-1	
 SmålandsVillan		TAKFOT INKLÄDD LÅNG 950mm -1 KAPAD TASS 687 HUSVÄGG 250 + SIDOB. 120 SKALA 1:45 SIDA 1/1	
RITAD/KONSTR. AV RNM	GRANSK 	ARBETSNR. ES020IL-1	
Stockholm. 2024-10-07 		KOD TYP POS ES020IL-1	RITNINGSNUMMER ES020IL-1
		REV.	

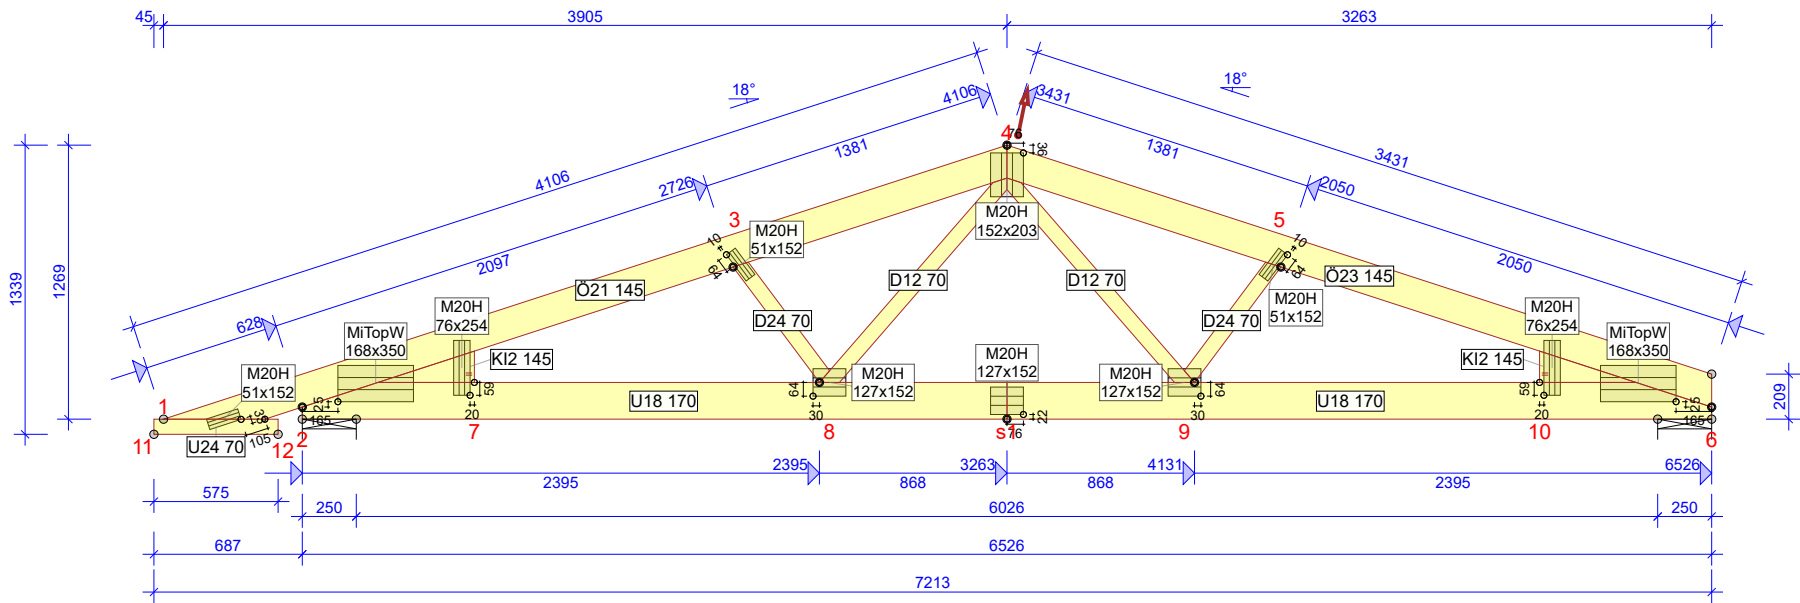

TOLERANS FÖRBANDSPACERING: 8 mm

2024-10-07 - 08:56
2024.2b (e327eed)

ARBETSNR.
ES020IL-1

KOD TYP POS

ES020IL-1

RITNINGSNUMMER

ES020IL-1

GRANSKAD AV: *TR*
RITAD/KONSTR. AV: RNM


OBOS BOSTADSUTVECKLING AB

ART NR: ES020IL-1

PRODUKTIONSRTNING


SIDA 1/1

TAKFOT INKLÄDD LÅNG 950mm -1 KAPAD TASS 687 REV.
HUSVÄGG 250 + SIDOB. 120

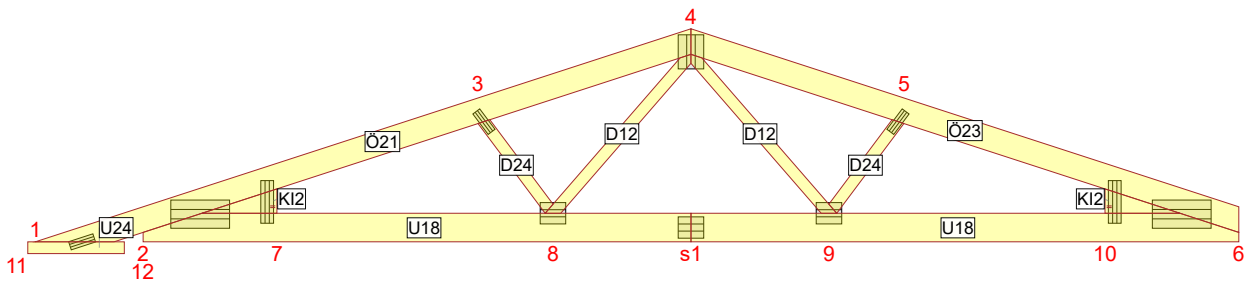


ÖVERRAM - Ö21

1-4	Dim./Kval	45 x 145 mm C24
	Total längd:	4106 mm
	ÖK / C / UK:	4106 / 3860 / 3613 mm
	Antal per konstruktion:	1 st
	Antal totalt:	1 st(1v)

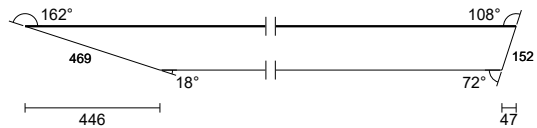


ÖVERRAM - Ö23

4-6	Dim./Kval	45 x 145 mm C24
	Total längd:	3478 mm
	ÖK / C / UK:	3431 / 3431 / 3431 mm
	Antal per konstruktion:	1 st
	Antal totalt:	1 st(1h)

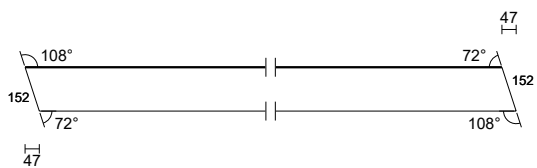

UNDERRAM - U18

s1-6	Dim./Kval	45 x 170 mm C24
2-s1	Total längd:	3263 mm
	ÖK / C / UK:	2912 / 3174 / 3263 mm
	Antal per konstruktion:	2 st
	Antal totalt:	2 st(1v,1h)

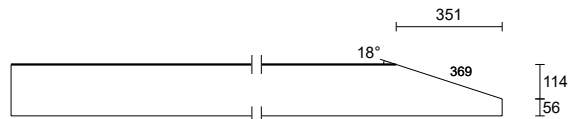


UNDERSPIKNING - U24

11-12	Dim./Kval	45 x 70 mm C18
	Total längd:	575 mm
	Antal per konstruktion:	1 st
	Antal totalt:	1 st(1v)




DIAGONAL - D12

4-8	Dim./Kval	45 x 70 mm C18
4-9	Total längd:	1284 mm
	ÖK / C / UK:	1183 / 1253 / 1226 mm
	Antal per konstruktion:	2 st
	Antal totalt:	2 st(1v,1h)

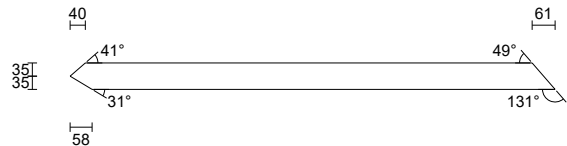


DIAGONAL - D24

3-8	Dim./Kval	45 x 70 mm C18
5-9	Total längd:	667 mm
	ÖK / C / UK:	628 / 648 / 667 mm
	Antal per konstruktion:	2 st
	Antal totalt:	2 st(1v,1h)

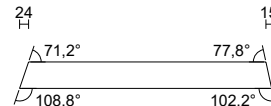

KIL - KI2

2-7	Dim./Kval	45 x 145 mm C24
10-6	Total längd:	446 mm
	ÖK / C / UK:	0 / 223 / 446 mm
	Antal per konstruktion:	2 st
	Antal totalt:	2 st(1v,1h)

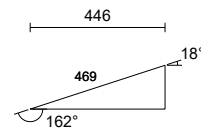

ARBETSNR.

ES020IL-1

GRANSKAD AV:

RITAD/KONSTR. AV: RNM

KAPLISTA

SIDA 1/1

2024-10-07 - 08:56
2024.2b (e327eed)

KOD TYP POS

ES020IL-1

RITNINGSNUMMER
ES020IL-1

OBOS BOSTADSUTVECKLING AB
ART NR: ES020IL-1

TAKFOT INKLÄDD LÄNG 950mm -1 KAPAD TASS 687 REV.
HUSVÄGG 250 + SIDOB. 120

