

ALLMÄNNA ANVISNINGAR

KONSTRUKTIONEN HAR BERÄKNATS MED
DATAPROGRAM "MITEK PAMIR",
OBOS Bostadsutveckling AB - LIC.NR: 1514
DIM. NORM: EN 1995-1-1:2004 + A2:2014 + EKS 12
FULLSTÄNDIGA RESULTAT ENL. BERÄKNINGSUTSKRIFT

GENERELLA UPPGIFTER

MATERIALBREDD (mm):	45
VIKT (kg/st):	61
LASTBREDD MAX (mm):	1200
LASTFÖRDELNINGSAKTOR:	1,1
SÄKERHETSKLASS:	SK2
KLIMATKLASS:	2 = 65% <= RF < 85%
AVSTYVNINGAR: SE TVÄRSNITTSTABELL	

BELASTNINGAR (kN/m²)


SNÖLAST (Sk, 400 m.ö.h.):	2,5
VINDLAST (qp(z)):	0,85
NYTTIG LAST PÅ UNDERRAM:	0,5
EGENLAST PÅ YTTERTAK:	0,65
EGENLAST PÅ INNERTAK:	0,3

UPPLAGSREAKTIONER BROTTGR. (kN)

KNUT NR	RIKTN.	LK P/L MAX	LK M MAX	LK K/MO MAX	LK K/MO MIN	U-BR mm
2	HOR.	0	0	-1,43	-	
2	VER.	5,56	21,62	19,08	-1,89	58
6	VER.	5,56	21,62	19,08	-1,89	58

MAX DEFORMATION I BRUKSGRÄNS (mm)

KNUT NR	VER.	HOR.	LK NR.
s1	8,5	0,7	1001:5:1 (WINST)
s1-10	8,4	0,8	1001:6:1 (WINST)
6	0,8	1,6	1001:5:1 (WINST)
FÖR DEFORMATION I FLER PUNKTER - SE BER.UTSKRIFT			

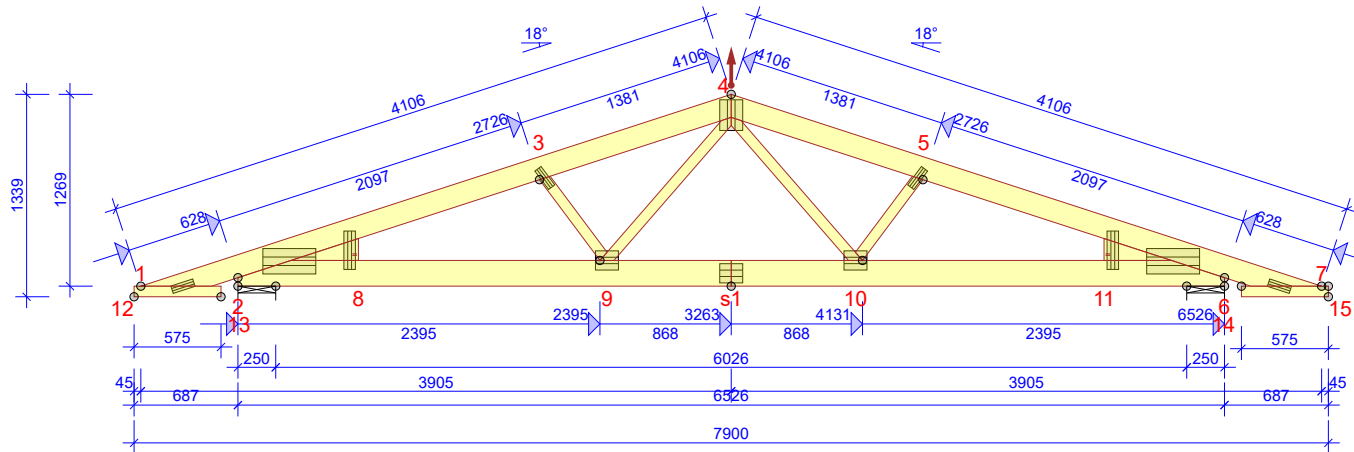


TOLERANS FÖRBANDSPACERING: 8 mm

TVÄRSNITT BREDD 45 mm					FÖRBAND - EXKL. SKARVAR				
KONSTR. DEL	HÖJD mm	KVALITET	AVSTYV. mm/st	NG. %	KNUT NR	FÖRB. LITT	BREDD mm	LÄNGD mm	NG. %
1-4	145	C24	800	76	1	M20H	51	152	73
4-7	145	C24	800	76	2:1	MiTopW	168	350	49
2-6	170	C24	FULL	56	2:2	M20H	76	254	74
12-13	70	C18	INGEN	14	3	M20H	51	152	45
14-15	70	C18	INGEN	14	4	M20H	152	203	66
3-9	70	C18	INGEN	27	5	M20H	51	152	45
4-9	70	C18	INGEN	48	6:1	MiTopW	168	350	49
4-10	70	C18	INGEN	48	6:2	M20H	76	254	74
5-10	70	C18	INGEN	27	7	M20H	51	152	73
2-8	145	C24		28	9	M20H	127	152	64
6-11	145	C24		28	10	M20H	127	152	64

FÖRBAND - SKARVAR				
KNUT NR	FÖRB. LITT	BREDD mm	LÄNGD mm	NG. %
s1	M20H	127	152	89

© Ritningen är skyddad enligt upphovsrättslagen och får inte kopieras, spridas eller i övrigt användas utan upphovsmannens medgivande.

				OBOS BOSTADSUTVECKLING AB	
		RITAD/KONSTR. AV GRANSK ARBETSNR.		ART NR: ES020IL	
Stockholm. 2024-10-07		ES020IL		TAKFOT INKLÄDD LÅNG 950mm	
2024-10-07 - 08:56 2024.2b (e327eed)		HUSVÄGG 250 + SIDOB.		SKALA 1:50	SIDA 1/1
		KOD TYP POS		RITNINGNUMMER	
		ES020IL		ES020IL	
				REV.	

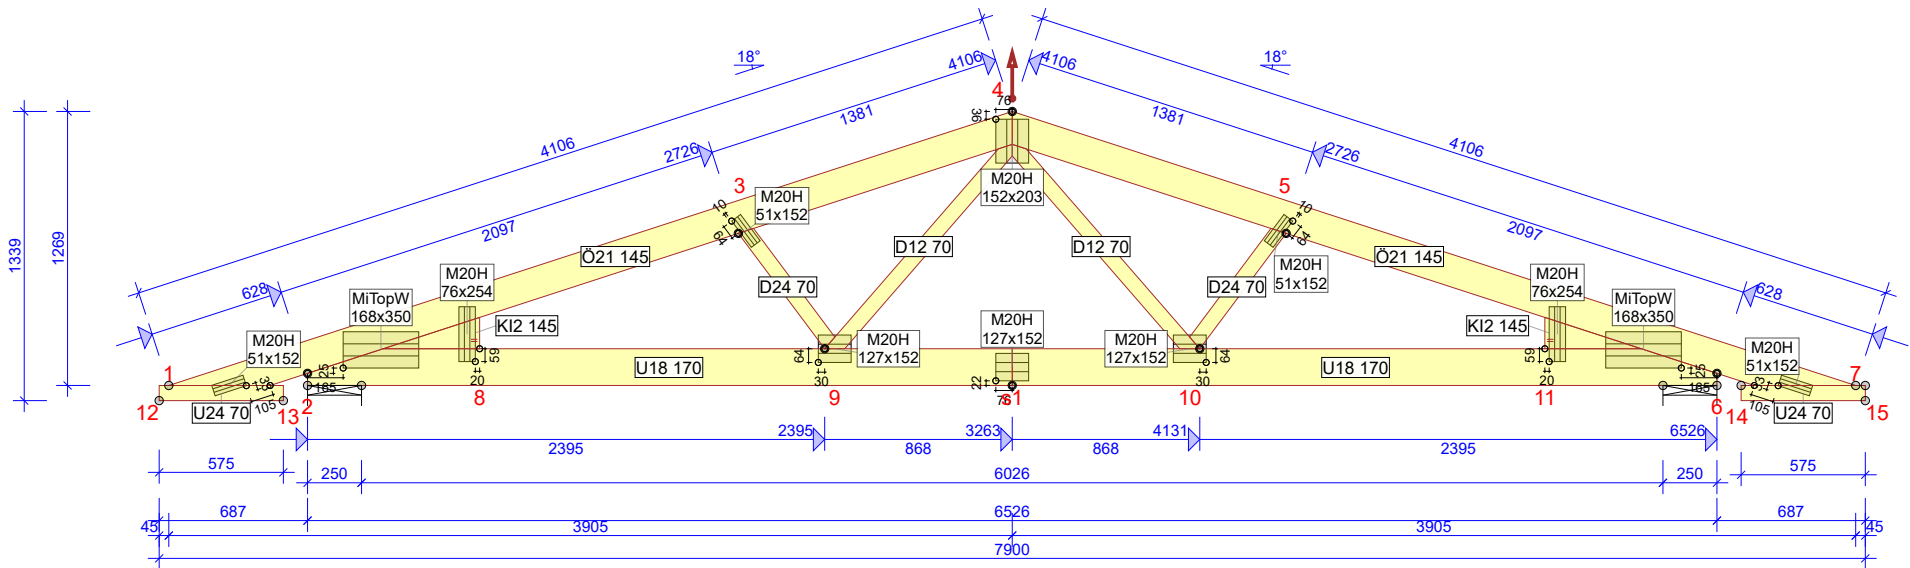

TOLERANS FÖRBANDSPACERING: 8 mm

2024-10-07 - 08:56
2024.2b (e327eed)

ARBETSNR.
ES020IL

KOD TYP POS
ES020IL

RITNINGSNUMMER
ES020IL


ART NR: ES020IL

GRANSKAD AV: *JR*
RITAD/KONSTR. AV: RNM

PRODUKTIONSRTNING


SIDA 1/1

TAKFOT INKLÄDD LÅNG 950mm REV.
HUSVÄGG 250 + SIDOB. 120

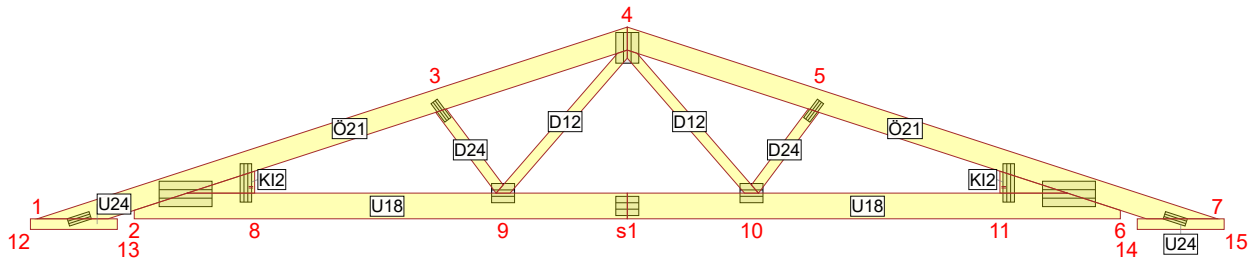


ÖVERRAM - Ö21

1-4	Dim./Kval	45 x 145 mm C24
7-4	Total längd:	4106 mm
	ÖK / C / UK:	4106 / 3860 / 3613 mm
	Antal per konstruktion:	2 st
	Antal totalt:	2 st(1v,1h)

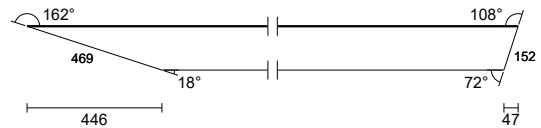

UNDERRAM - U18

s1-6	Dim./Kval	45 x 170 mm C24
2-s1	Total längd:	3263 mm
	ÖK / C / UK:	2912 / 3174 / 3263 mm
	Antal per konstruktion:	2 st
	Antal totalt:	2 st(1v,1h)

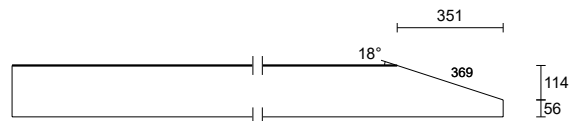


UNDERSPIKNING - U24

12-13	Dim./Kval	45 x 70 mm C18
14-15	Total längd:	575 mm
	Antal per konstruktion:	2 st
	Antal totalt:	2 st(1v,1h)




DIAGONAL - D12

4-9	Dim./Kval	45 x 70 mm C18
4-10	Total längd:	1284 mm
	ÖK / C / UK:	1183 / 1253 / 1226 mm
	Antal per konstruktion:	2 st
	Antal totalt:	2 st(1v,1h)

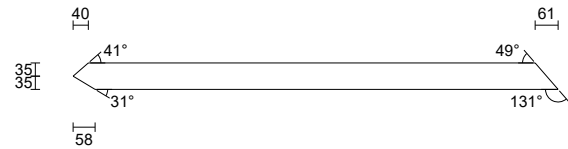

DIAGONAL - D24

3-9	Dim./Kval	45 x 70 mm C18
5-10	Total längd:	667 mm
	ÖK / C / UK:	628 / 648 / 667 mm
	Antal per konstruktion:	2 st
	Antal totalt:	2 st(1v,1h)

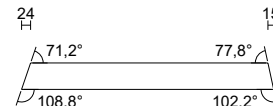

KIL - KI2

2-8	Dim./Kval	45 x 145 mm C24
11-6	Total längd:	446 mm
	ÖK / C / UK:	0 / 223 / 446 mm
	Antal per konstruktion:	2 st
	Antal totalt:	2 st(1v,1h)

